



CONCEPT, NOT FOR FABRICATION

LaneSkiff · github.com/BoujeeEnjinia1701/laneskiff

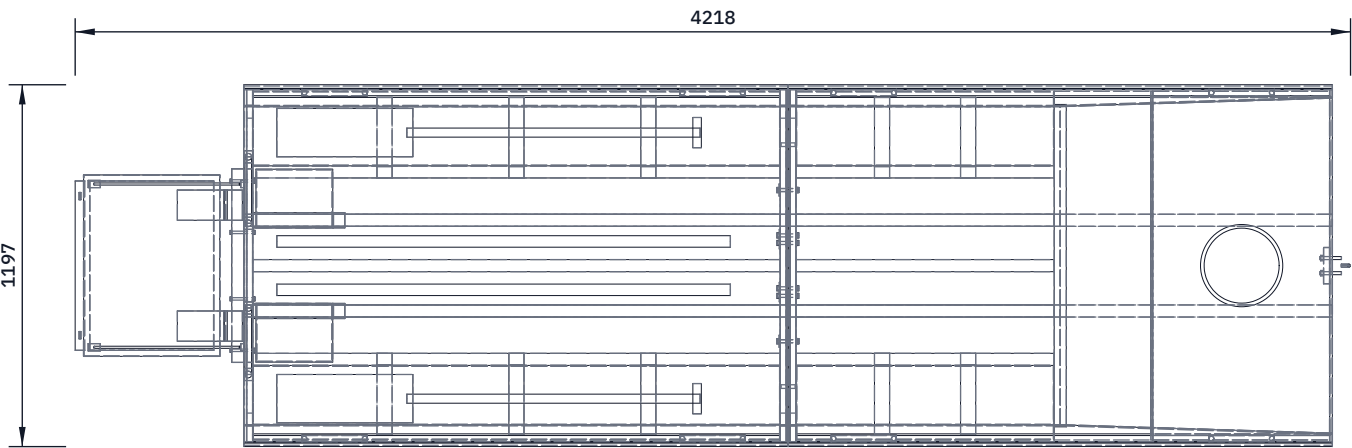


TOP VIEW

Scale 1:25; looking down (along -Z)

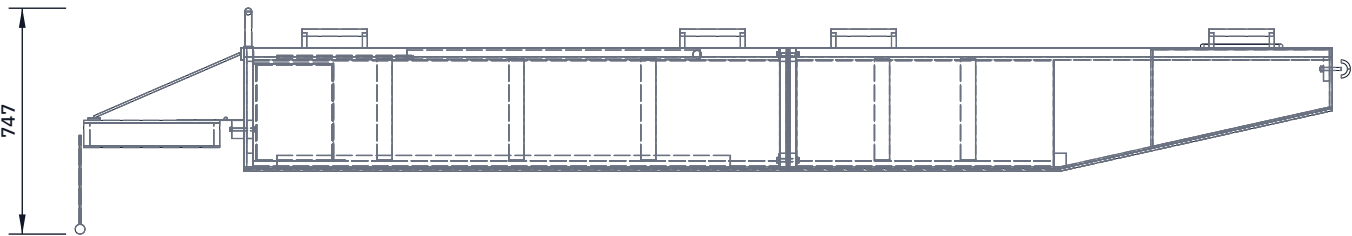

FRONT VIEW


Scale 1:25; looking at the front (along +Y)

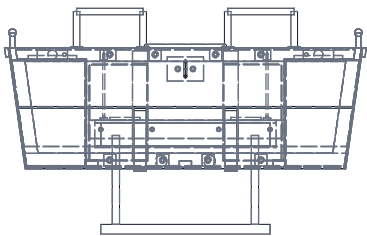

RIGHT VIEW

Scale 1:25; looking at the right side (along -X)

REV	DESCRIPTION	DATE	BY
P1	Preliminary GA for TRL 3 (from cad/src/model.py)	2026-10-03	AC
P2	LSK-DDR-002: design for construction	2026-10-03	AC
P3	LSK-DDR-003: light timber, bottom 60 wider, 4 mm sides, stern quarter foam	2026-10-03	AC

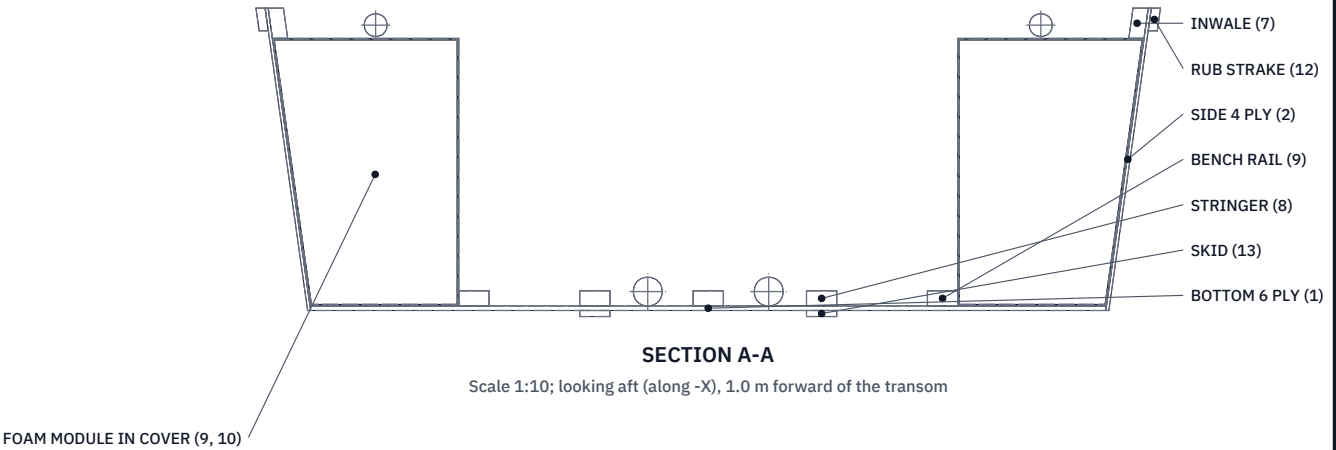

MAIN SIZES AND FIGURES (MM UNLESS STATED)

Length 3,600 in two halves of 1,800; beam overall 1,197
Depth 400; bottom 1,060 wide at the chine; sides flared 8 deg
Bottom flat to 2,700 from the transom, raked to 200 at the bow
Each half closed by its own bulkhead; joint: 8 M10 x 80 bolts
Bench modules 330 from the centreline to the side, top 360
Stern step float 450 x 600 x 90, hinged 40 behind the rail
Kick rung 270 below the float; stop straps at 20 deg down
Stern quarter foam 2 x 15 L, 250 clear way between (29)
Rated load 5 persons (375 kg); see LSK-CAL-001 for drafts
Third-angle; X from transom, Y to port; (n) = BOM line

LANESKIFF

github.com/BoujeeEnjinia1701/laneskiff

Two-piece flood rescue skiff: general arrangement

DRAWING NO.

LSK-DWG-001

REV

P3

SHEET

1 of 1

SIZE

ANSI B

SCALE

1:25

UNITS

mm

PROJECTION



DATE

2026-10-03

DRAWN

Amish Chadha

MATERIAL / NOTES

Okoume plywood, softwood framing and epoxy; parts per bom/bom.csv. PRELIMINARY, NOT FOR FABRICATION

Licensed CERN-OHL-S-2.0 · Design Molecule Lab · designmolecule.com

Generated from cad/src; do not edit by hand